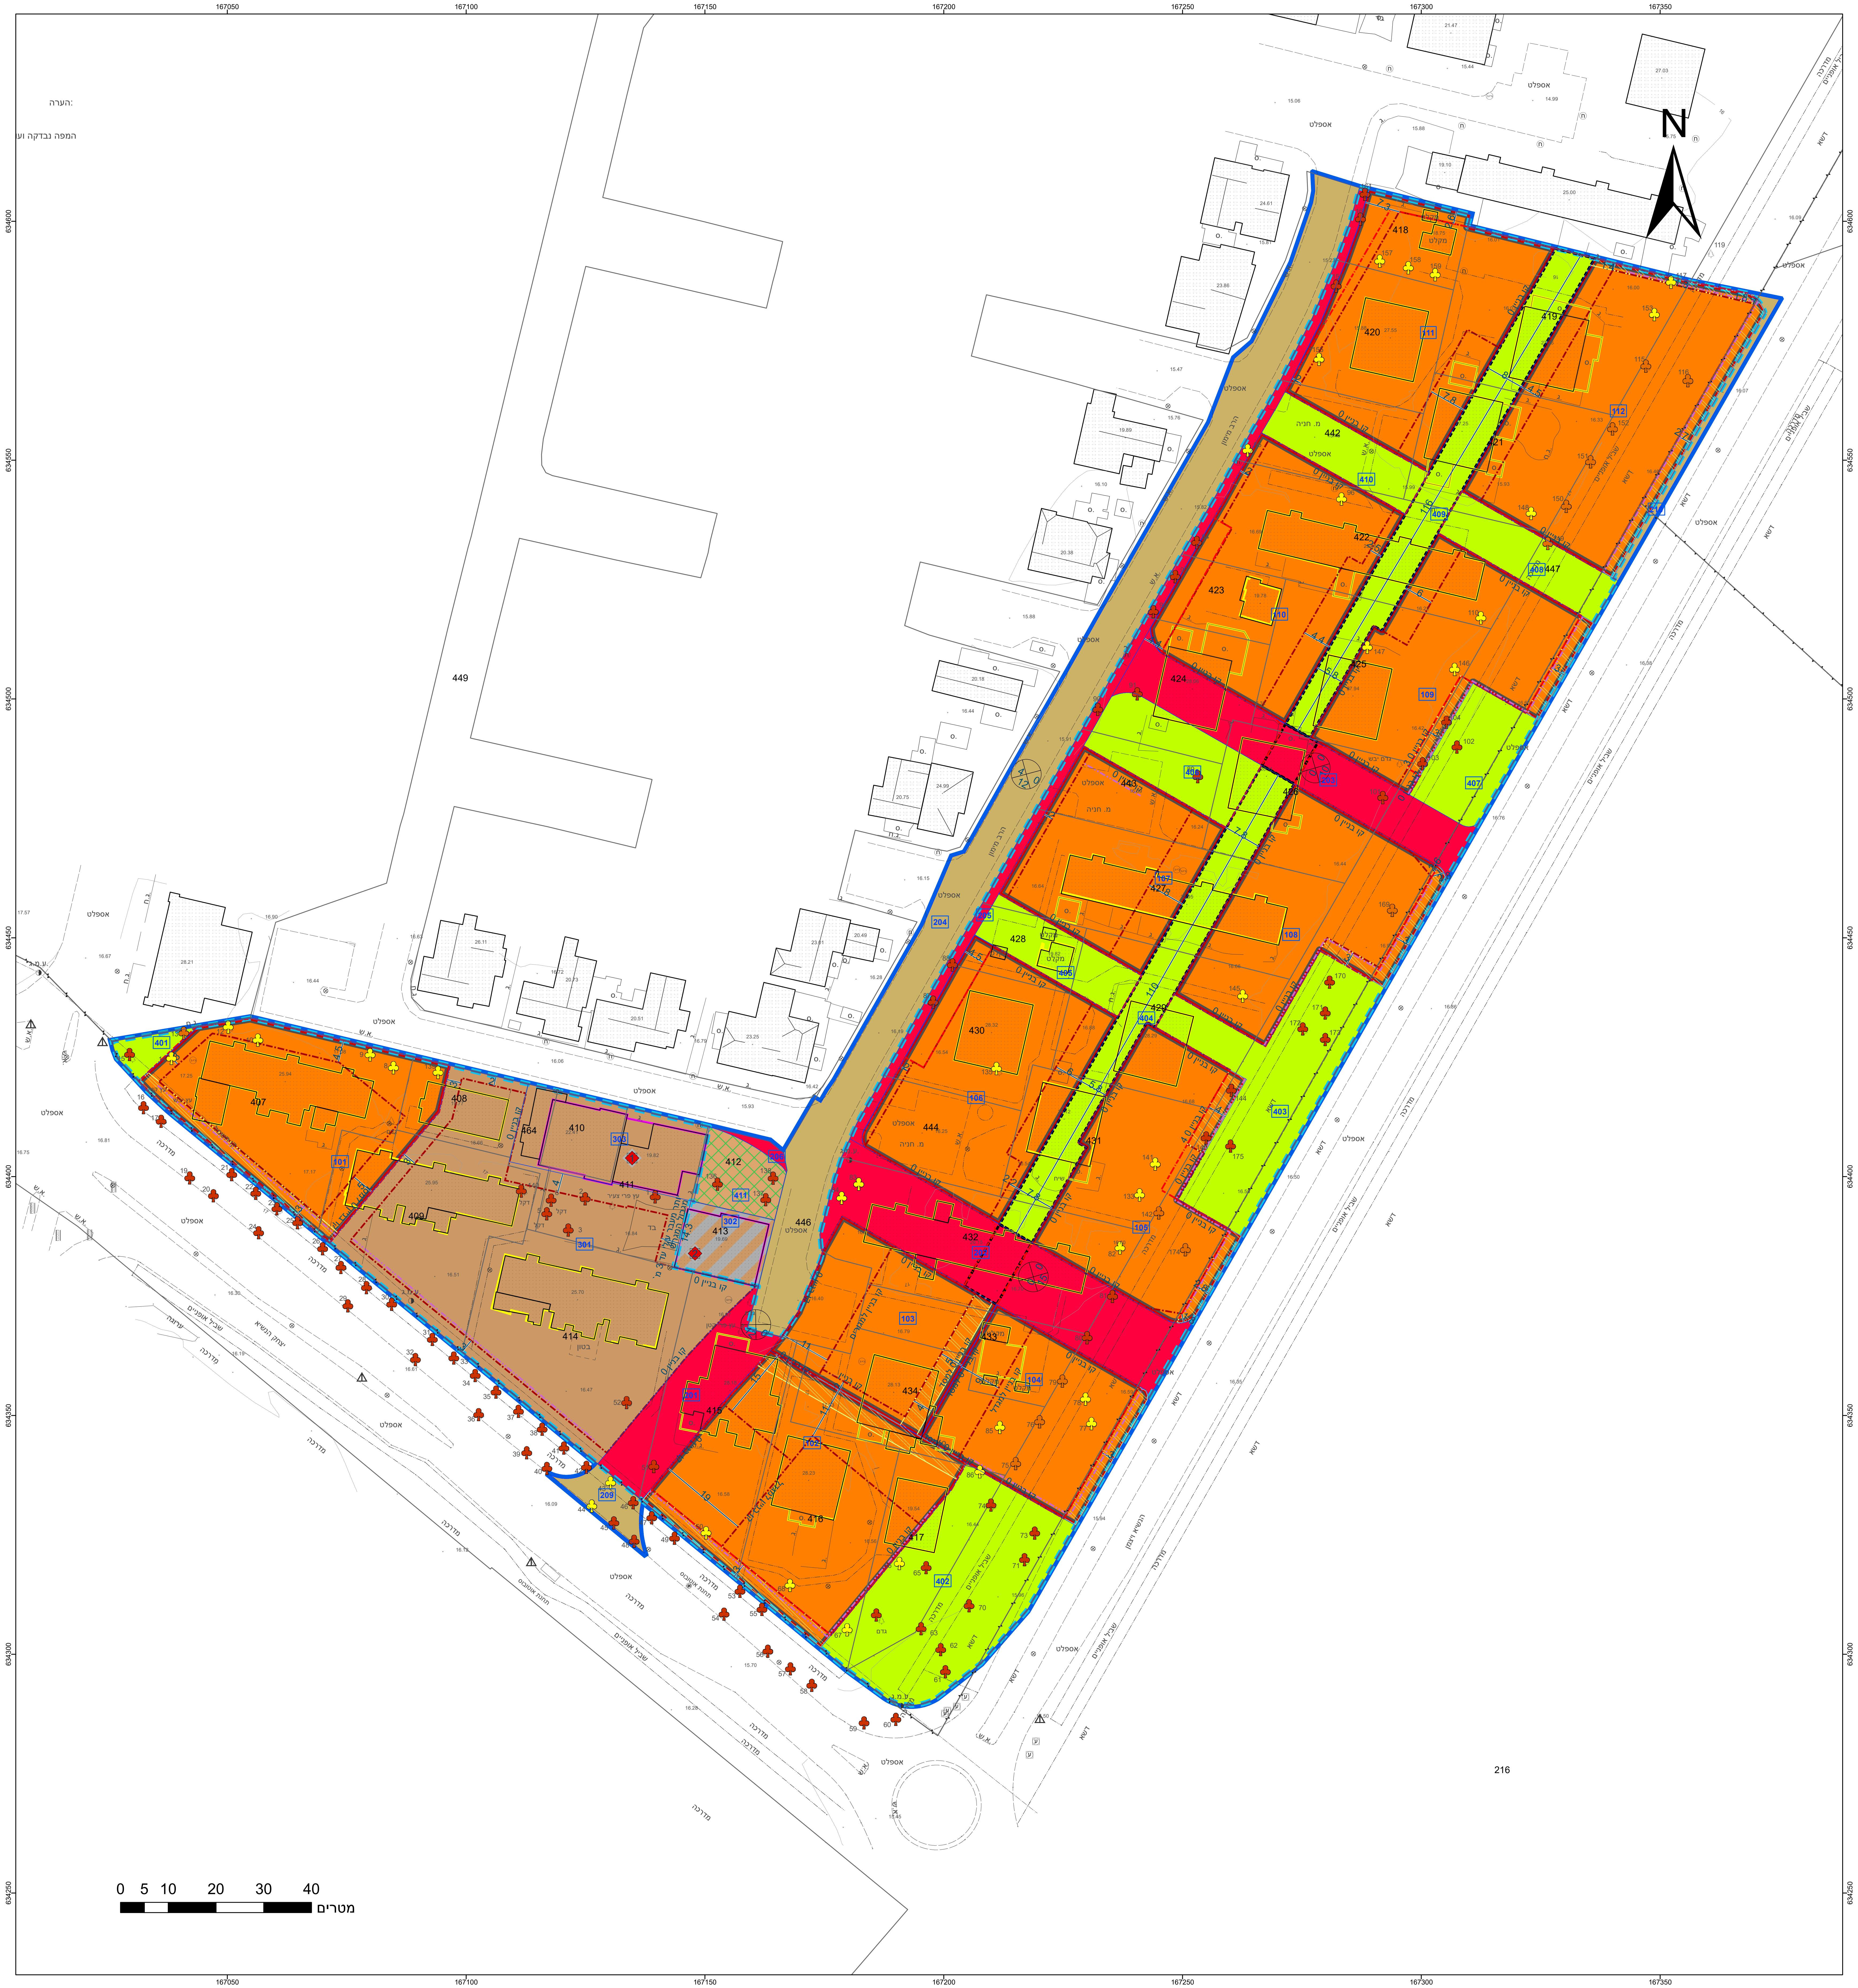

מקרא

▭	גבול תכנית
140	תא שטח ומספרו
גוש 1234	גבול גוש ומספרו
5	גבול חלקה ומספרה

רוזטת דרך: 1 – מספר הדרך; 2 – קוי בנין; 3 – רוחב הדרך

🟧	מגורים ה
🟫	מבנים ומוסדות ציבור
🟩	שטח ציבורי פתוח
▨	ככר עירונית
🟫	דרך מאושרת
🟥	דרך מוצעת
▨	מסחר ומבנים ומוסדות צבור
▨	זכות מעבר למעבר רגלי
⬚	שטח לאיחוד וחלוקה חדשה
▭	מבנה לשימור
▭	מבנה להריסה
⬚	גבול מתחם תלת מימדי
-·-·-	קו-בנין
-·-·-	קו בנין תחתי/תת קרקעי
—	מידות
-·-·-	חזית פעילה
♣	עץ/עצים לשימור
♣	עץ/עצים להעתקה
♣	עץ/עצים לכריתה
◆	אתר לשימור

תרשים התמצאות - קנ"מ 1:12000

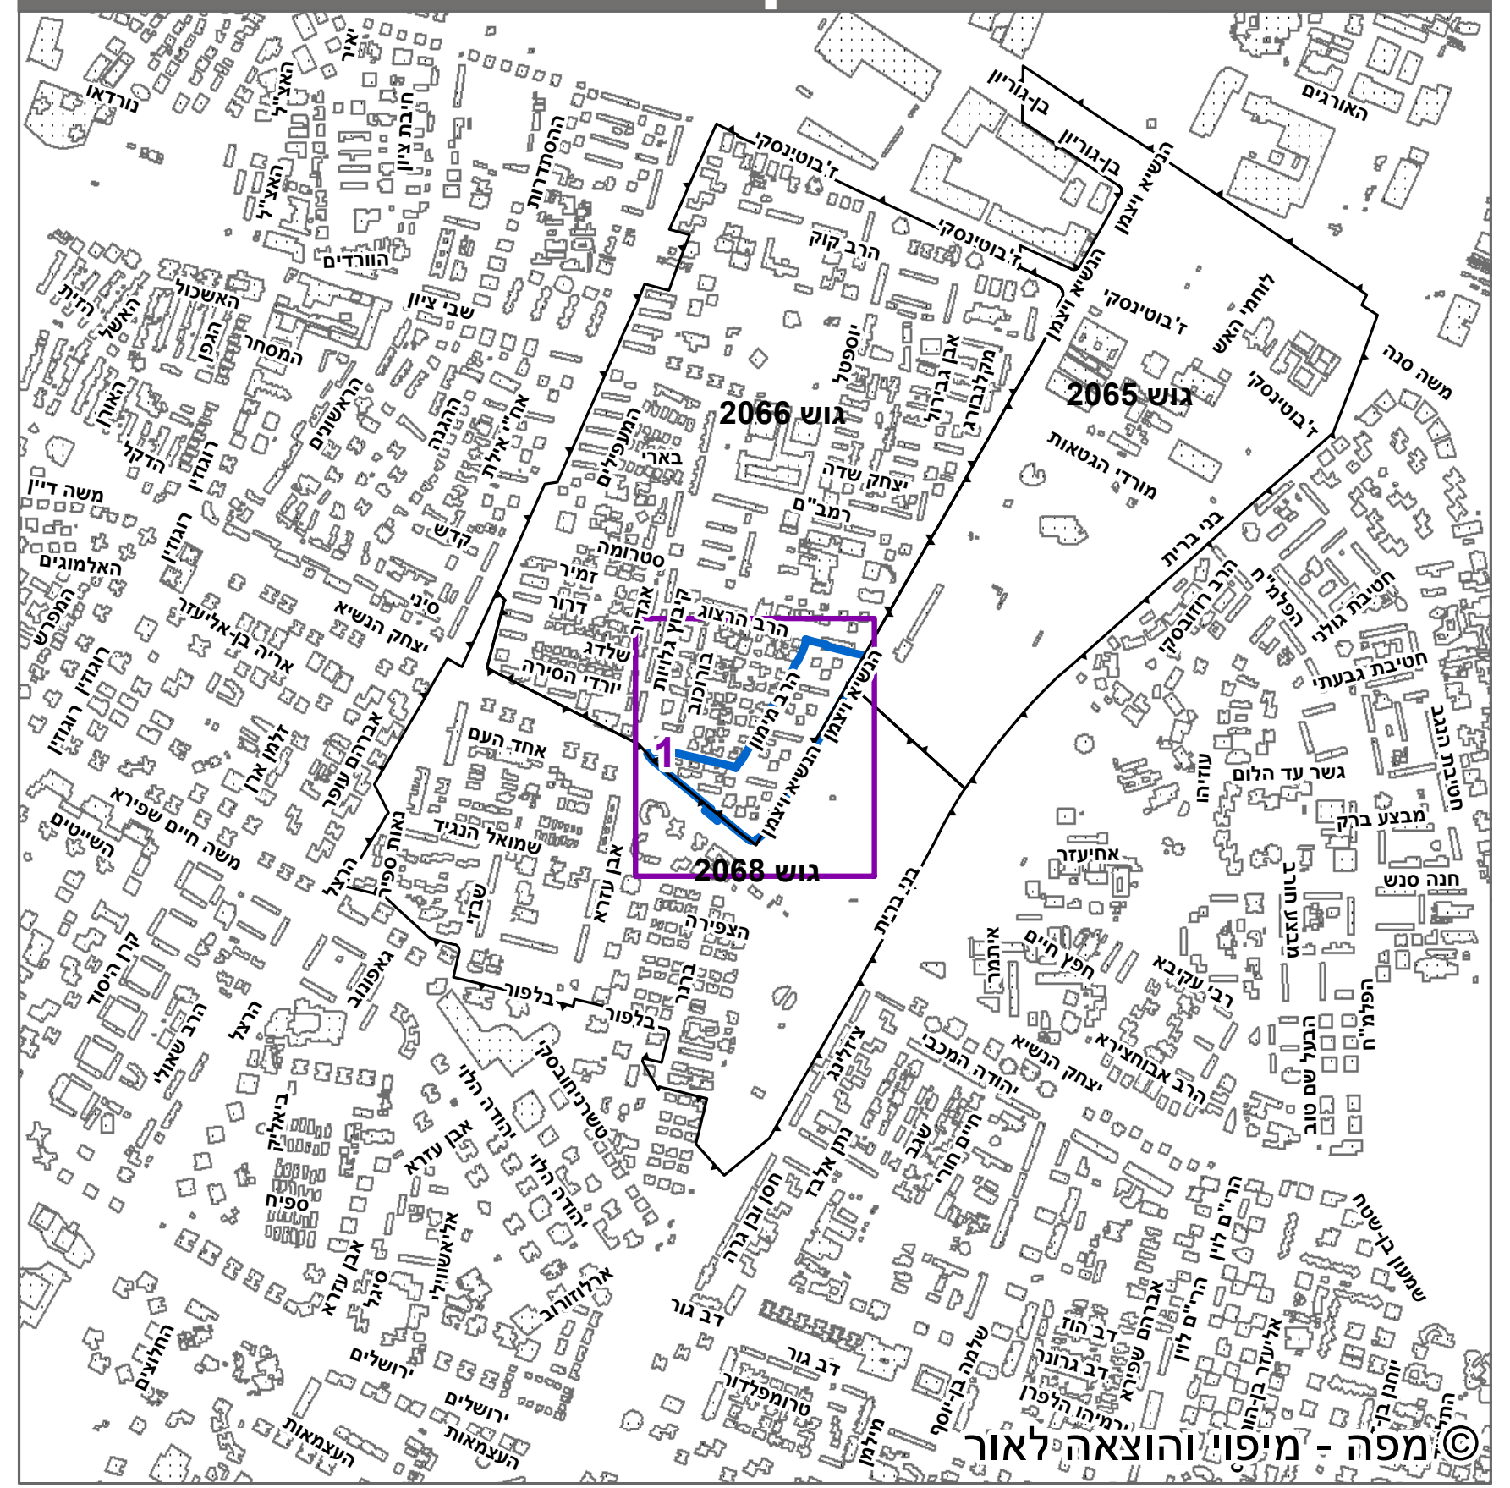

© מפה - מיפוי והוצאה לאור

שנת צילום אויר: 2023

תרשים סביבה - קנ"מ 1:3000

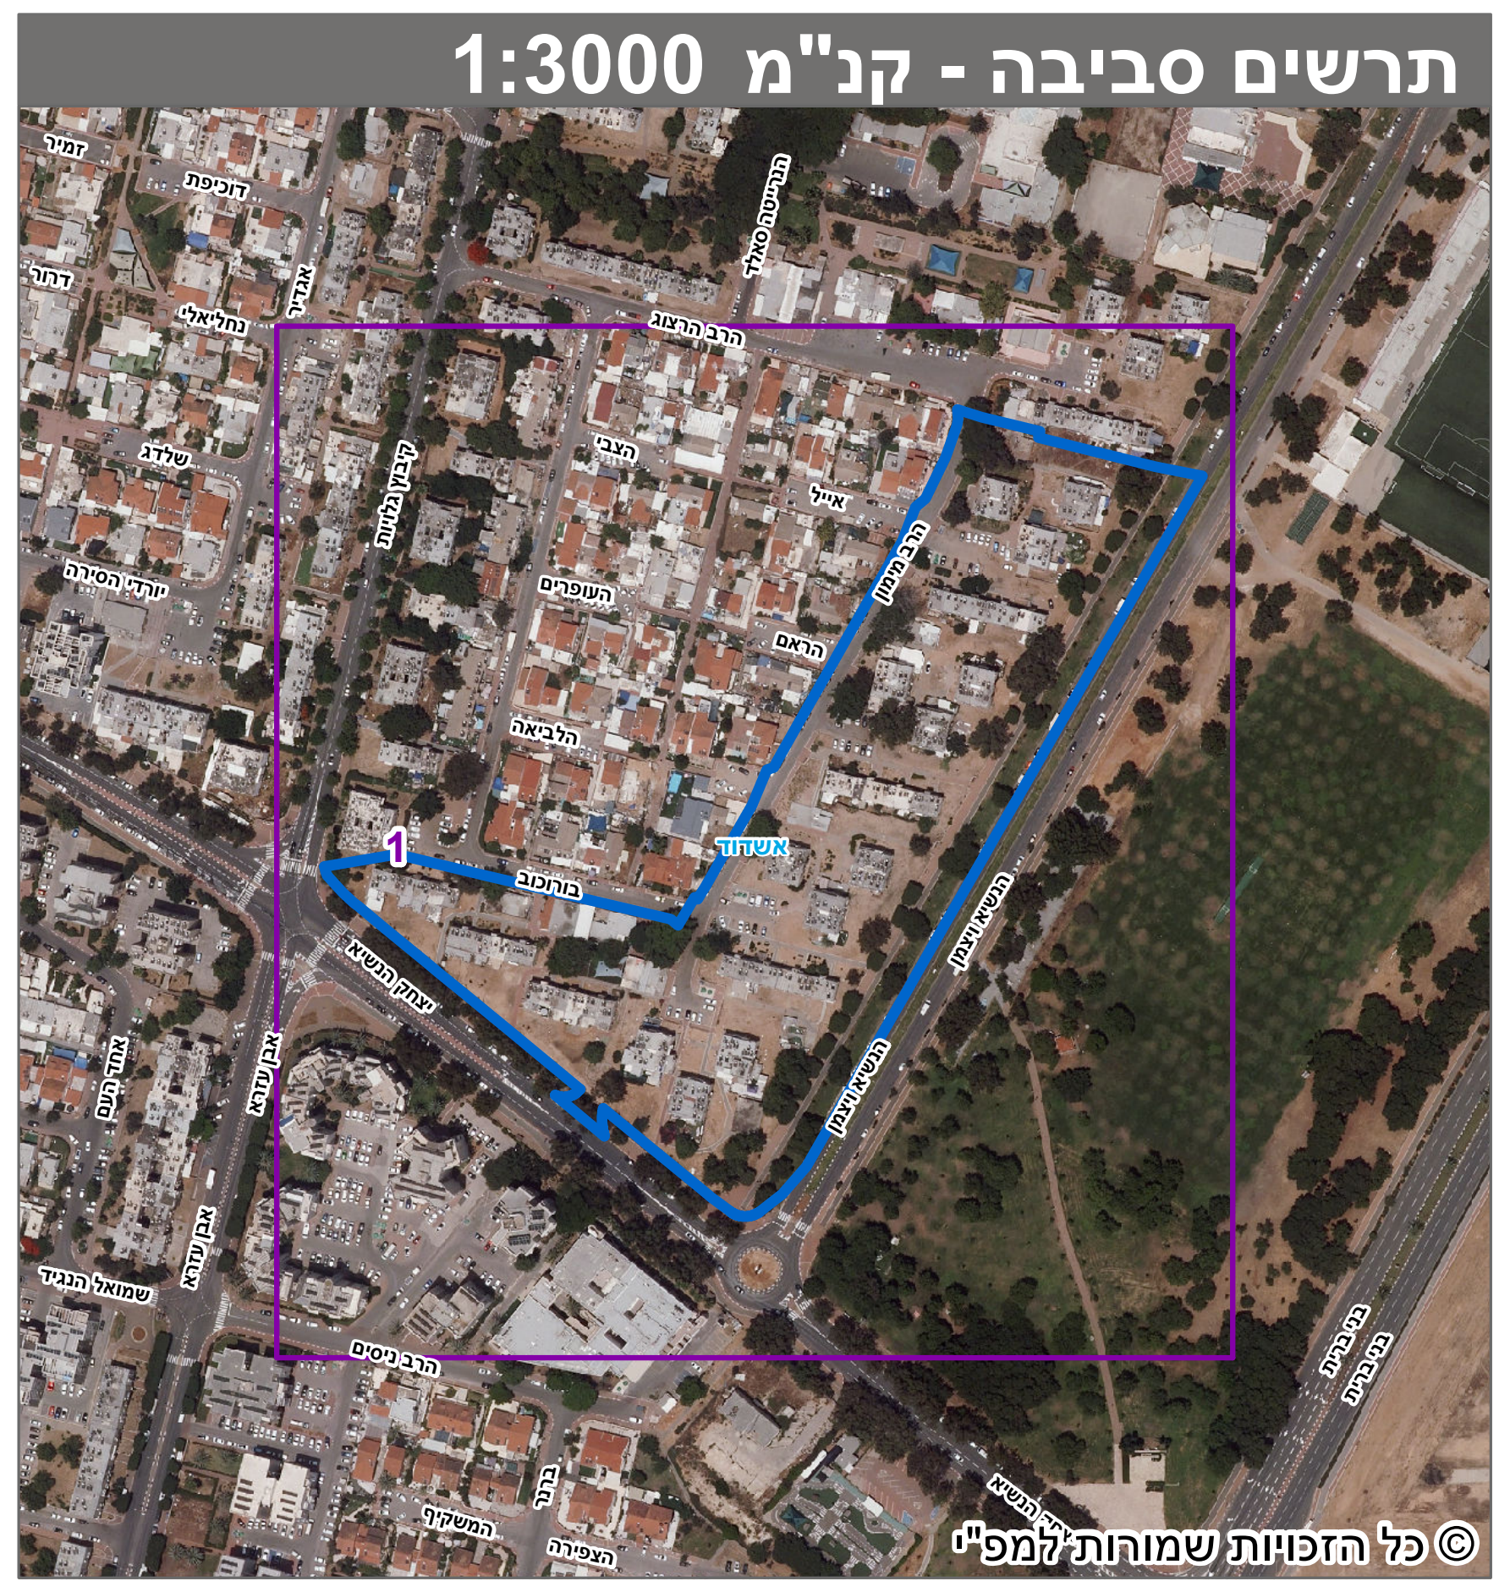

© כל הזכויות שמורות למפ"י

חוק לקידום הבנייה במתחמים מועדפים (הוראת שעה), התשע"ד-2014

תכנית מועדפת לדיור

מס' תמל/ 2047

פינוי בינוי הרב מימון רובע ב'
אשדוד

תשריט מצב מוצע גיליון 1 מתוך 1

מחוז	**דרום**
מרחב תכנון מקומי	**אשדוד**
רשות מקומית	**אשדוד**
ישוב	**אשדוד**
תכנית בסמכות	ארצית
איחוד וחלוקה	איחוד ו/או חלוקה ללא הסכמת כל הבעלים בכל תחום התכנית/בחלק מתחום התכנית
היתרים או הרשאות	תכנית שמכוחה ניתן להוציא היתרים או הרשאות
מונה תדפיס התשריט	54
מועד הפקה	13/11/2025 18:14
שטח התכנית	36.114 דונם
קנה מידה	1:500

אישורים בתכנית מס' תמל/ 2047

מינהל התכנון
החוק לקידום הבניה במתחמים
מועדפים לדיור(הוראת שעה)
התשע"ד,2014 הועדה למתחמים
מועדפים לדיור החליטה ביום
05/11/2025
לאשר את התכנית
01/12/2025
יו"ר הועדה למתחמים מועדפים לדיור

שמות*

מגיש התכנית	**רשות מקומית** תאגיד: **עיריית אשדוד**
מגיש התכנית	תאגיד: **ספיר התחדשות עירונית בע"מ**
עורך ראשי	**גיל מינסטר** תאגיד: **גיל מינסטר אדריכלים**
יזם	תאגיד: **ספיר התחדשות עירונית בע"מ**

טבלת גושים וחלקות*

מספר גוש	חלק/ כל הגוש	מספרי חלקות בשלמותן	מספרי חלקות בחלקיותן
2065	חלק		32
2066	חלק	407-434, 442-444, 464	446-447
2068	חלק		216

הריני מצהיר בזאת כי המפה הטופוגרפית/המצבית המהווה רקע לתכנית זו, נערכה על ידי ביום 25.08.2024 והיא הוכנה לפי הוראות נוהל מבא"ת ובהתאם להוראות החוק ולתקנות המודדים שבתוקף.
דיוק הקו הכחול והקדסטר: מדידה אנליטית מלאה ברמת תצ"ר

שם המודד	מספר רשיון	חתימה	תאריך
יאיר נחמיאס מודד מוסמך	603		

---

* הרשימה המלאה מפורטת בהוראות התכנית / בהודעה שפורסמה בעיתונות וברשומות